
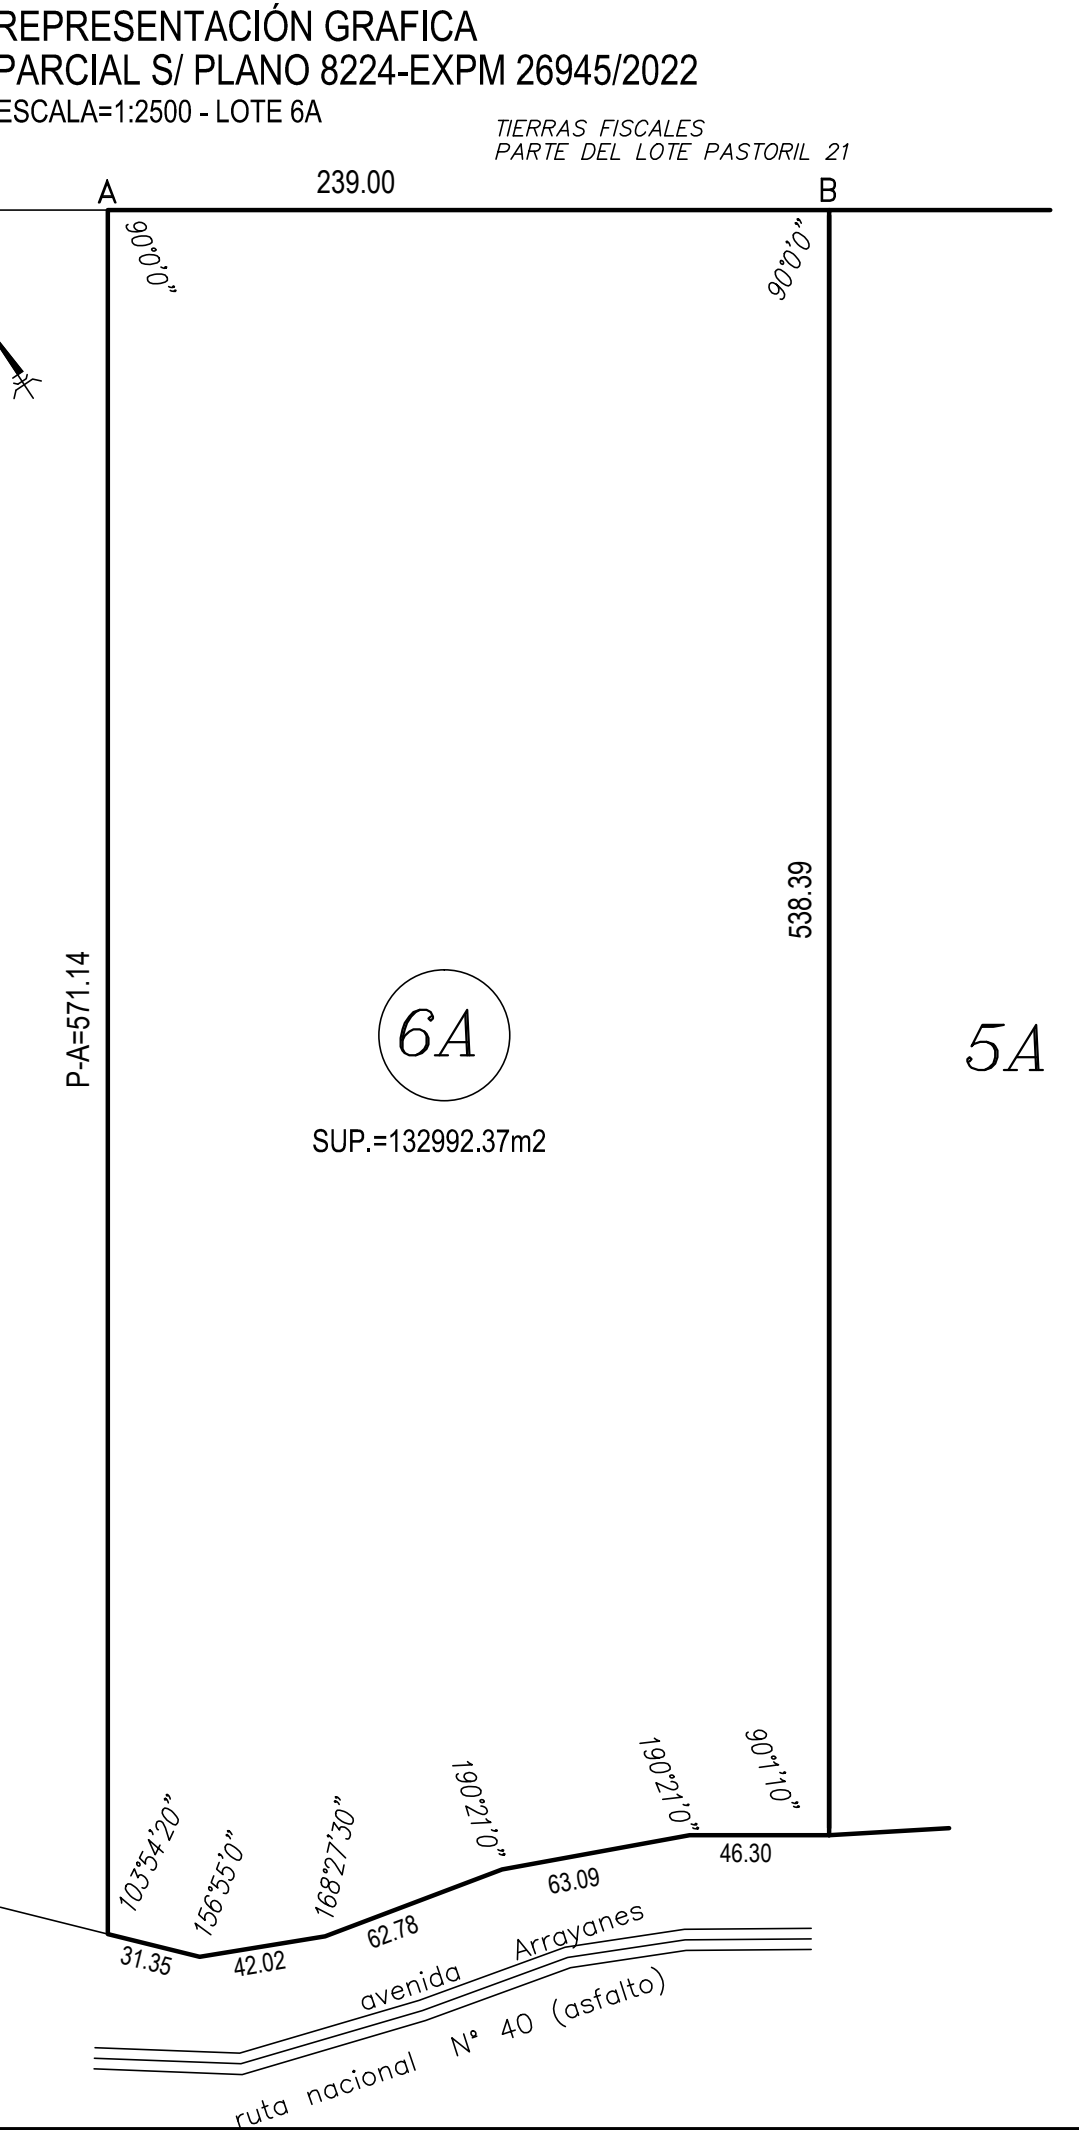


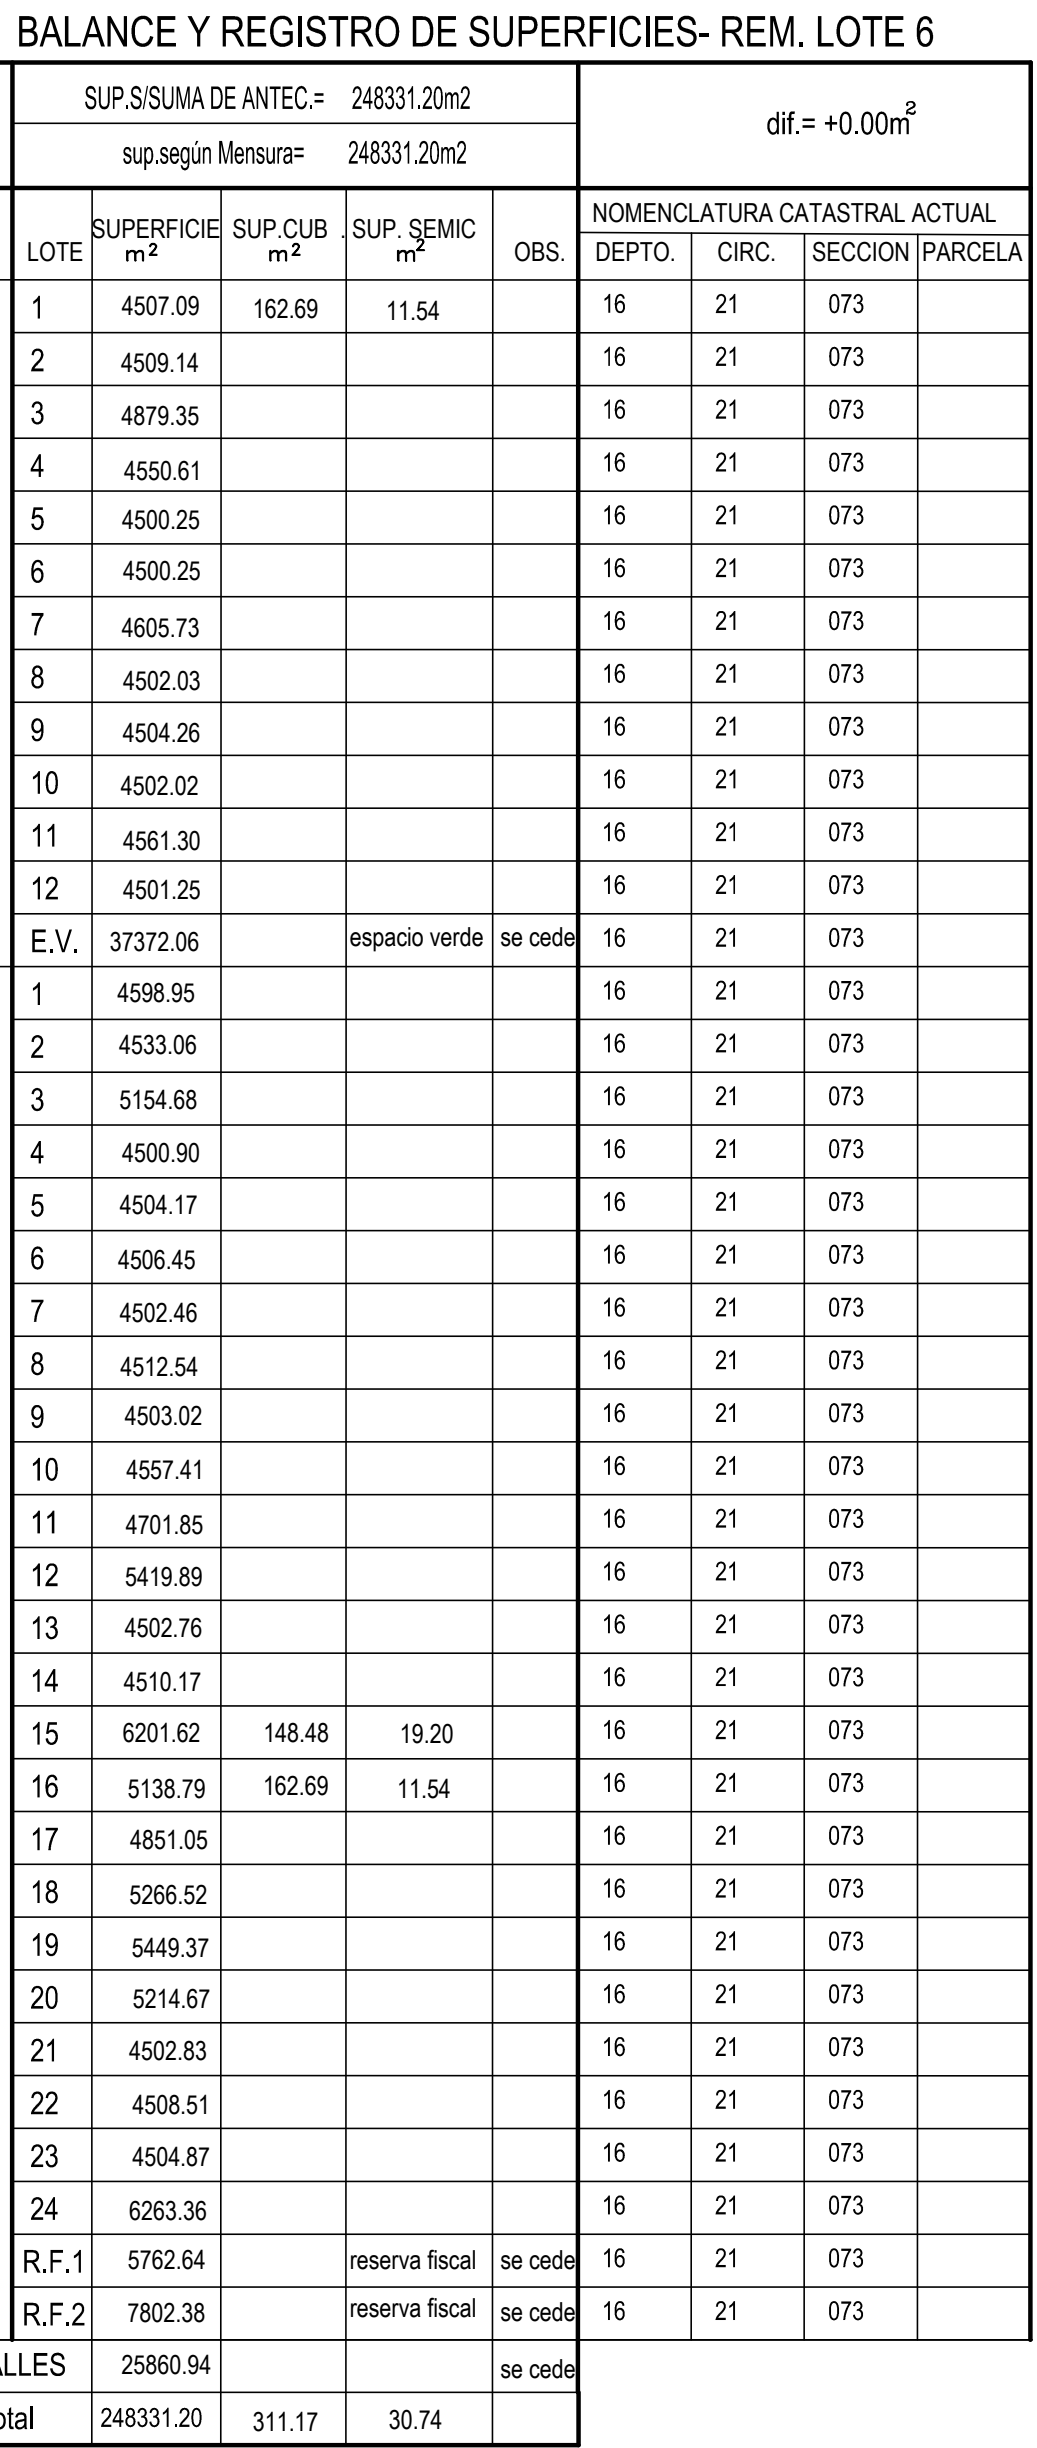

PROVINCIA DEL NEUQUEN
DEPARTAMENTO: LOS LAGOS
LOCALIDAD: VILLA LA ANGOSTURA
MENSURA PARTICULAR CON UNIFICACION Y FRACCIONAMIENTO
DE LOS LOTES 5A Y 6A DEL LOTE PASTORIL 21

PROPIETARIOS:

JUAN ANTONIO BALLESTER	MARIA JACINTA BALLESTER
JOSÉ FRANCISCO BALLESTER	SANTIAGO BALLESTER

NOMENCLATURA CATASTRAL DE ORIGEN	16-21-073-7144-0000 (Lote 6A)
	16-21-073-5664-0000 (Lote 5A)

ANTECEDENTES	INSCRIPCION EN EL REGISTRO DE LA PROPIEDAD INMUEBLE
LEGALES: TÍTULO DE PROPIEDAD	MATRICULA 1746-LOS LAGOS (LOTE 6-Fr. Mayor)
TECNICOS: 8224-EXPM 26945/2022	MATRICULA 1747-LOS LAGOS (LOTE 5-Fr Mayor)

CROQUIS DE LOCALIZACION: PUERTA DE ESCALA	Propietarios:
--	---------------

8c

GABRIEL MOSES SALAMA
D.U.N.I.17.203.380
CERRO BAYO 49-VILLA LA ANZOZURA
(POR PODER)

OBSERVACIONES	
---------------	--

--	--

--	--

TABLE 1. *Continued*

Miguel Raerdonck van Megrode		
------------------------------	--	--

Mat. Prof. N°310AGR Calle Los Taiques 85 - Villa La Angostura	8224-EXPM	DE 1
--	-----------	------